


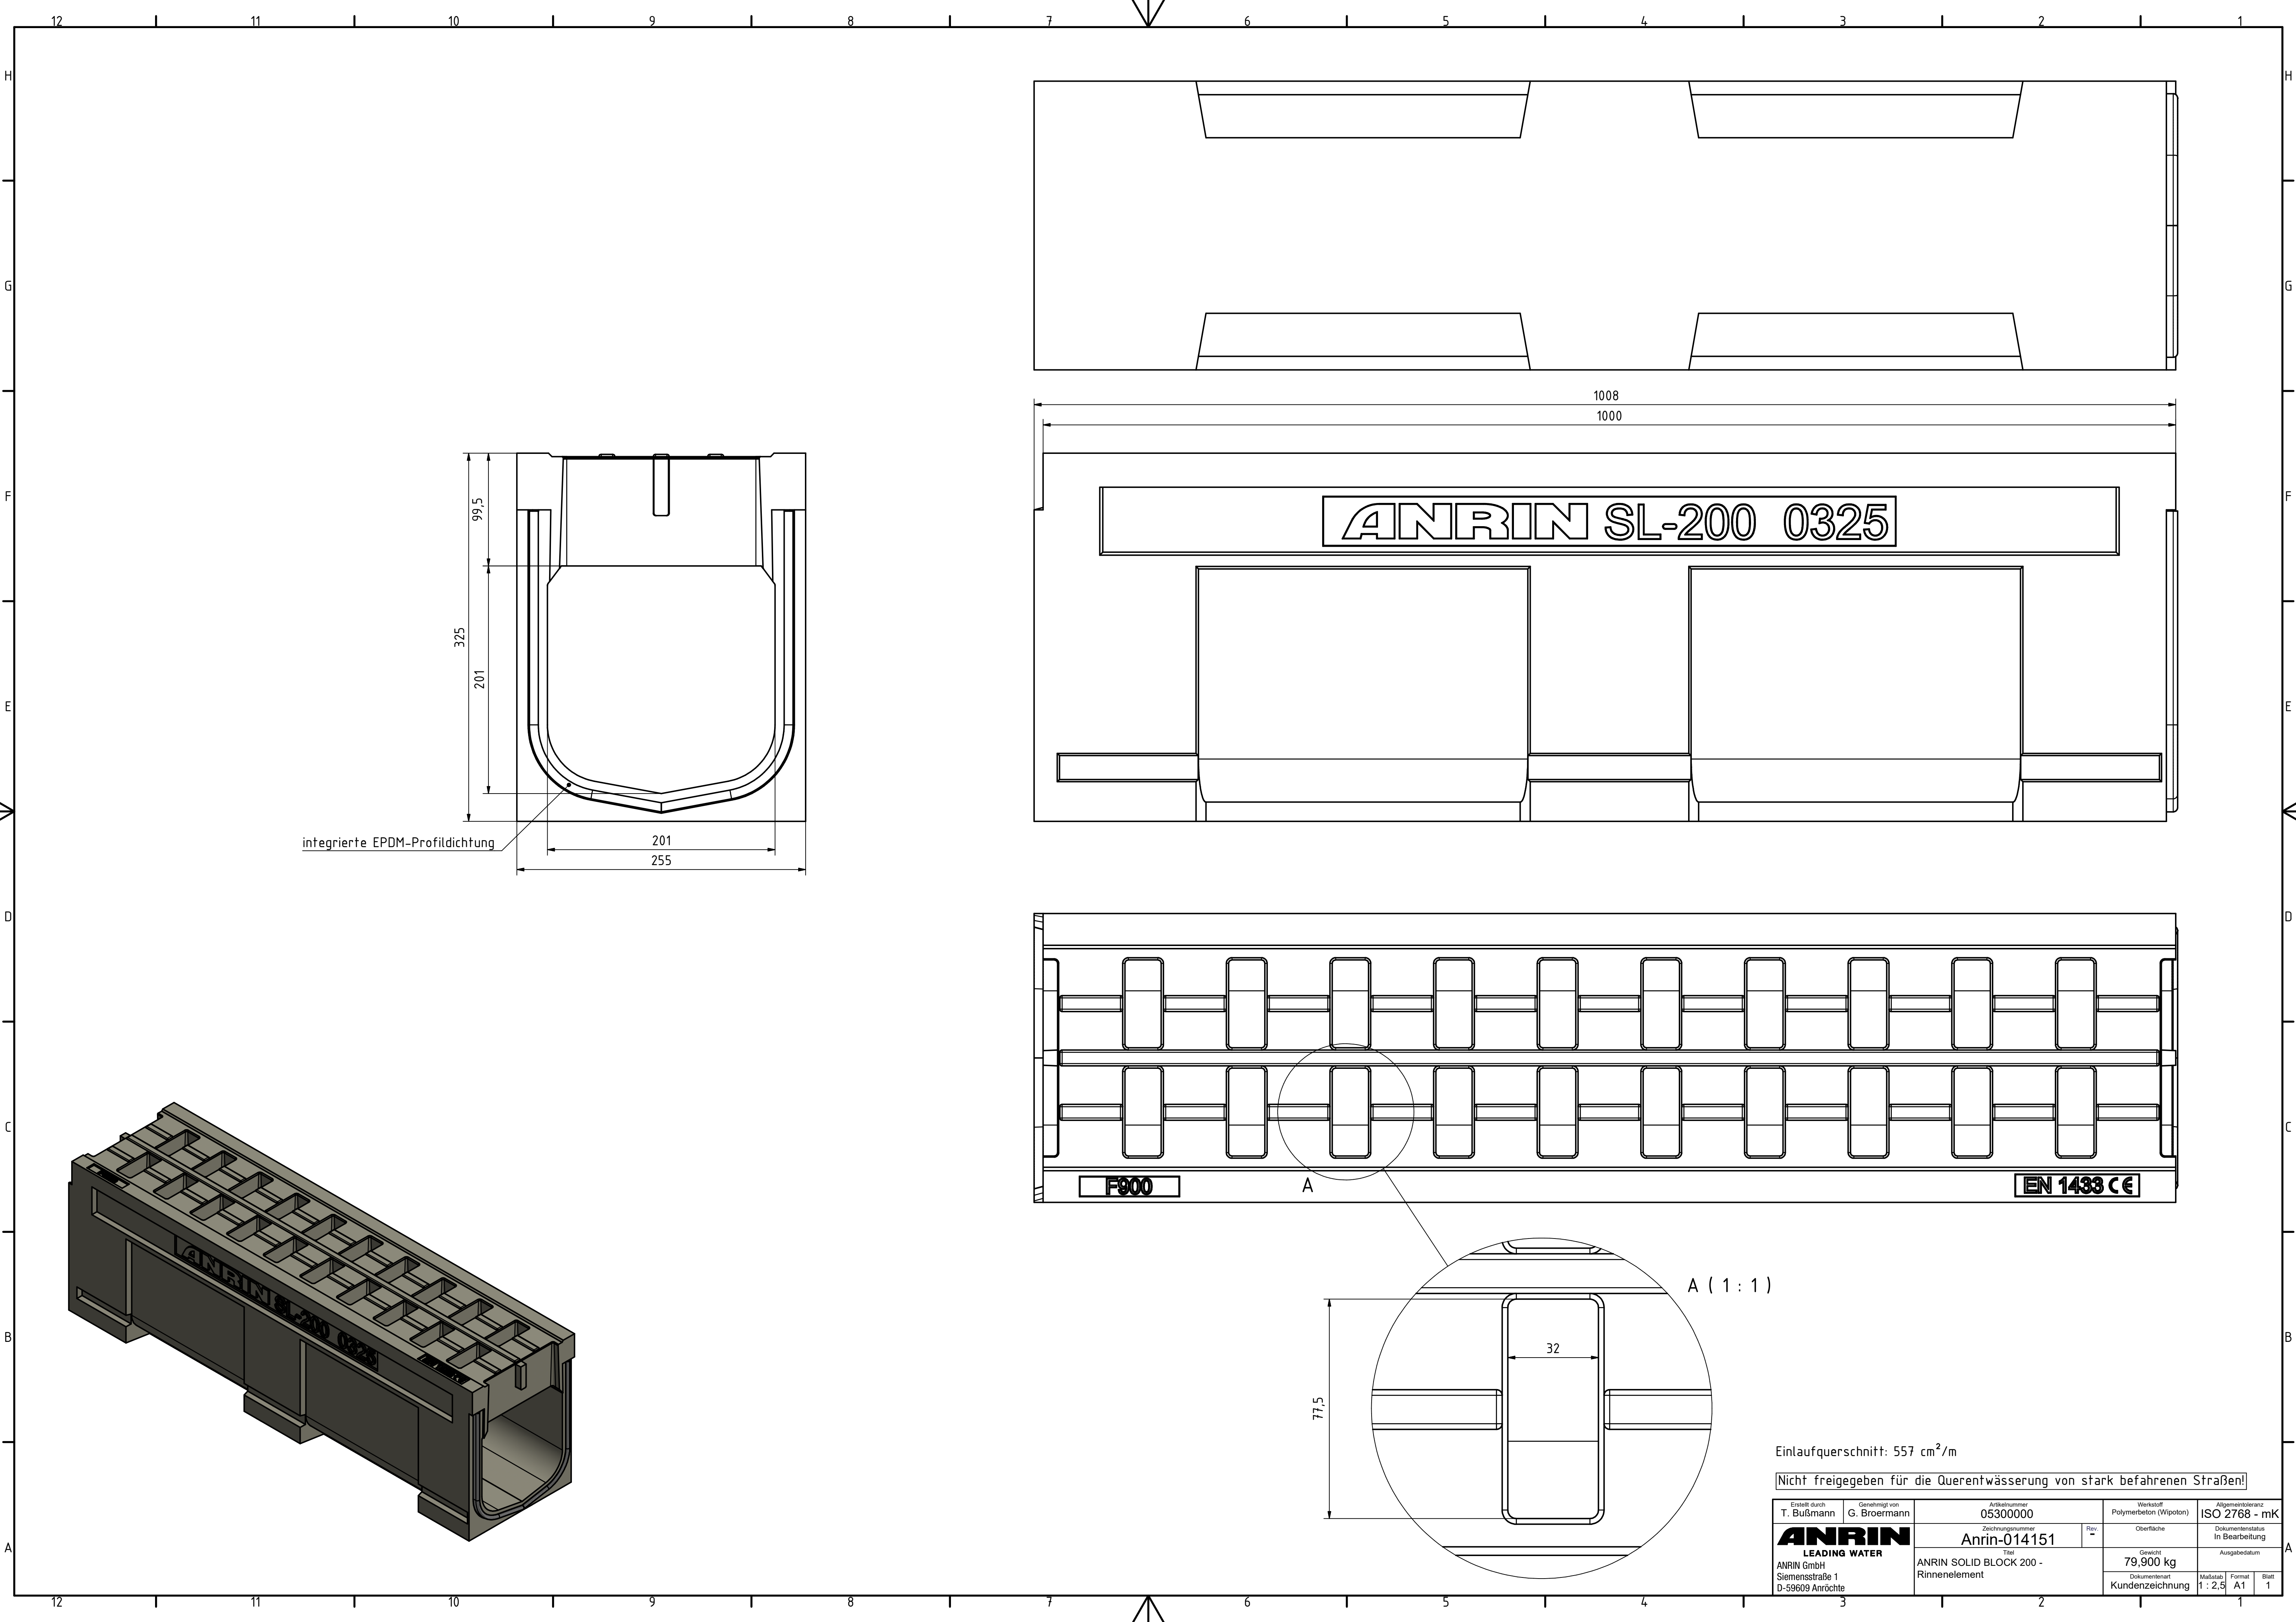

integrierte EPDM-Profilichtung

ANRIN SL-200 0325

F900

EN 1433 CE

A (1:1)

Einlaufquerschnitt: 557 cm²/m

Nicht freigegeben für die Querenwässerung von stark befahrenen Straßen!

Erstellt durch T. Bußmann	Genehmigt von G. Broermann	Artikelnummer 05300000	Werkstoff Polymerbeton (Wipolon)	Allgemeintoleranz ISO 2768 - mK
ANRIN LEADING WATER		Zeichnungsnummer Anrin-014151	Rev. -	Dokumentationsstatus In Bearbeitung
ANRIN GmbH Siemensstraße 1 D-59609 Anröchte		Gewicht 79,900 kg		Ausgabedatum
ANRIN SOLID BLOCK 200 - Rinnenelement		Dokumententyp Kundenzeichnung	Maßstab 1:2,5	Format A1
				Blatt 1